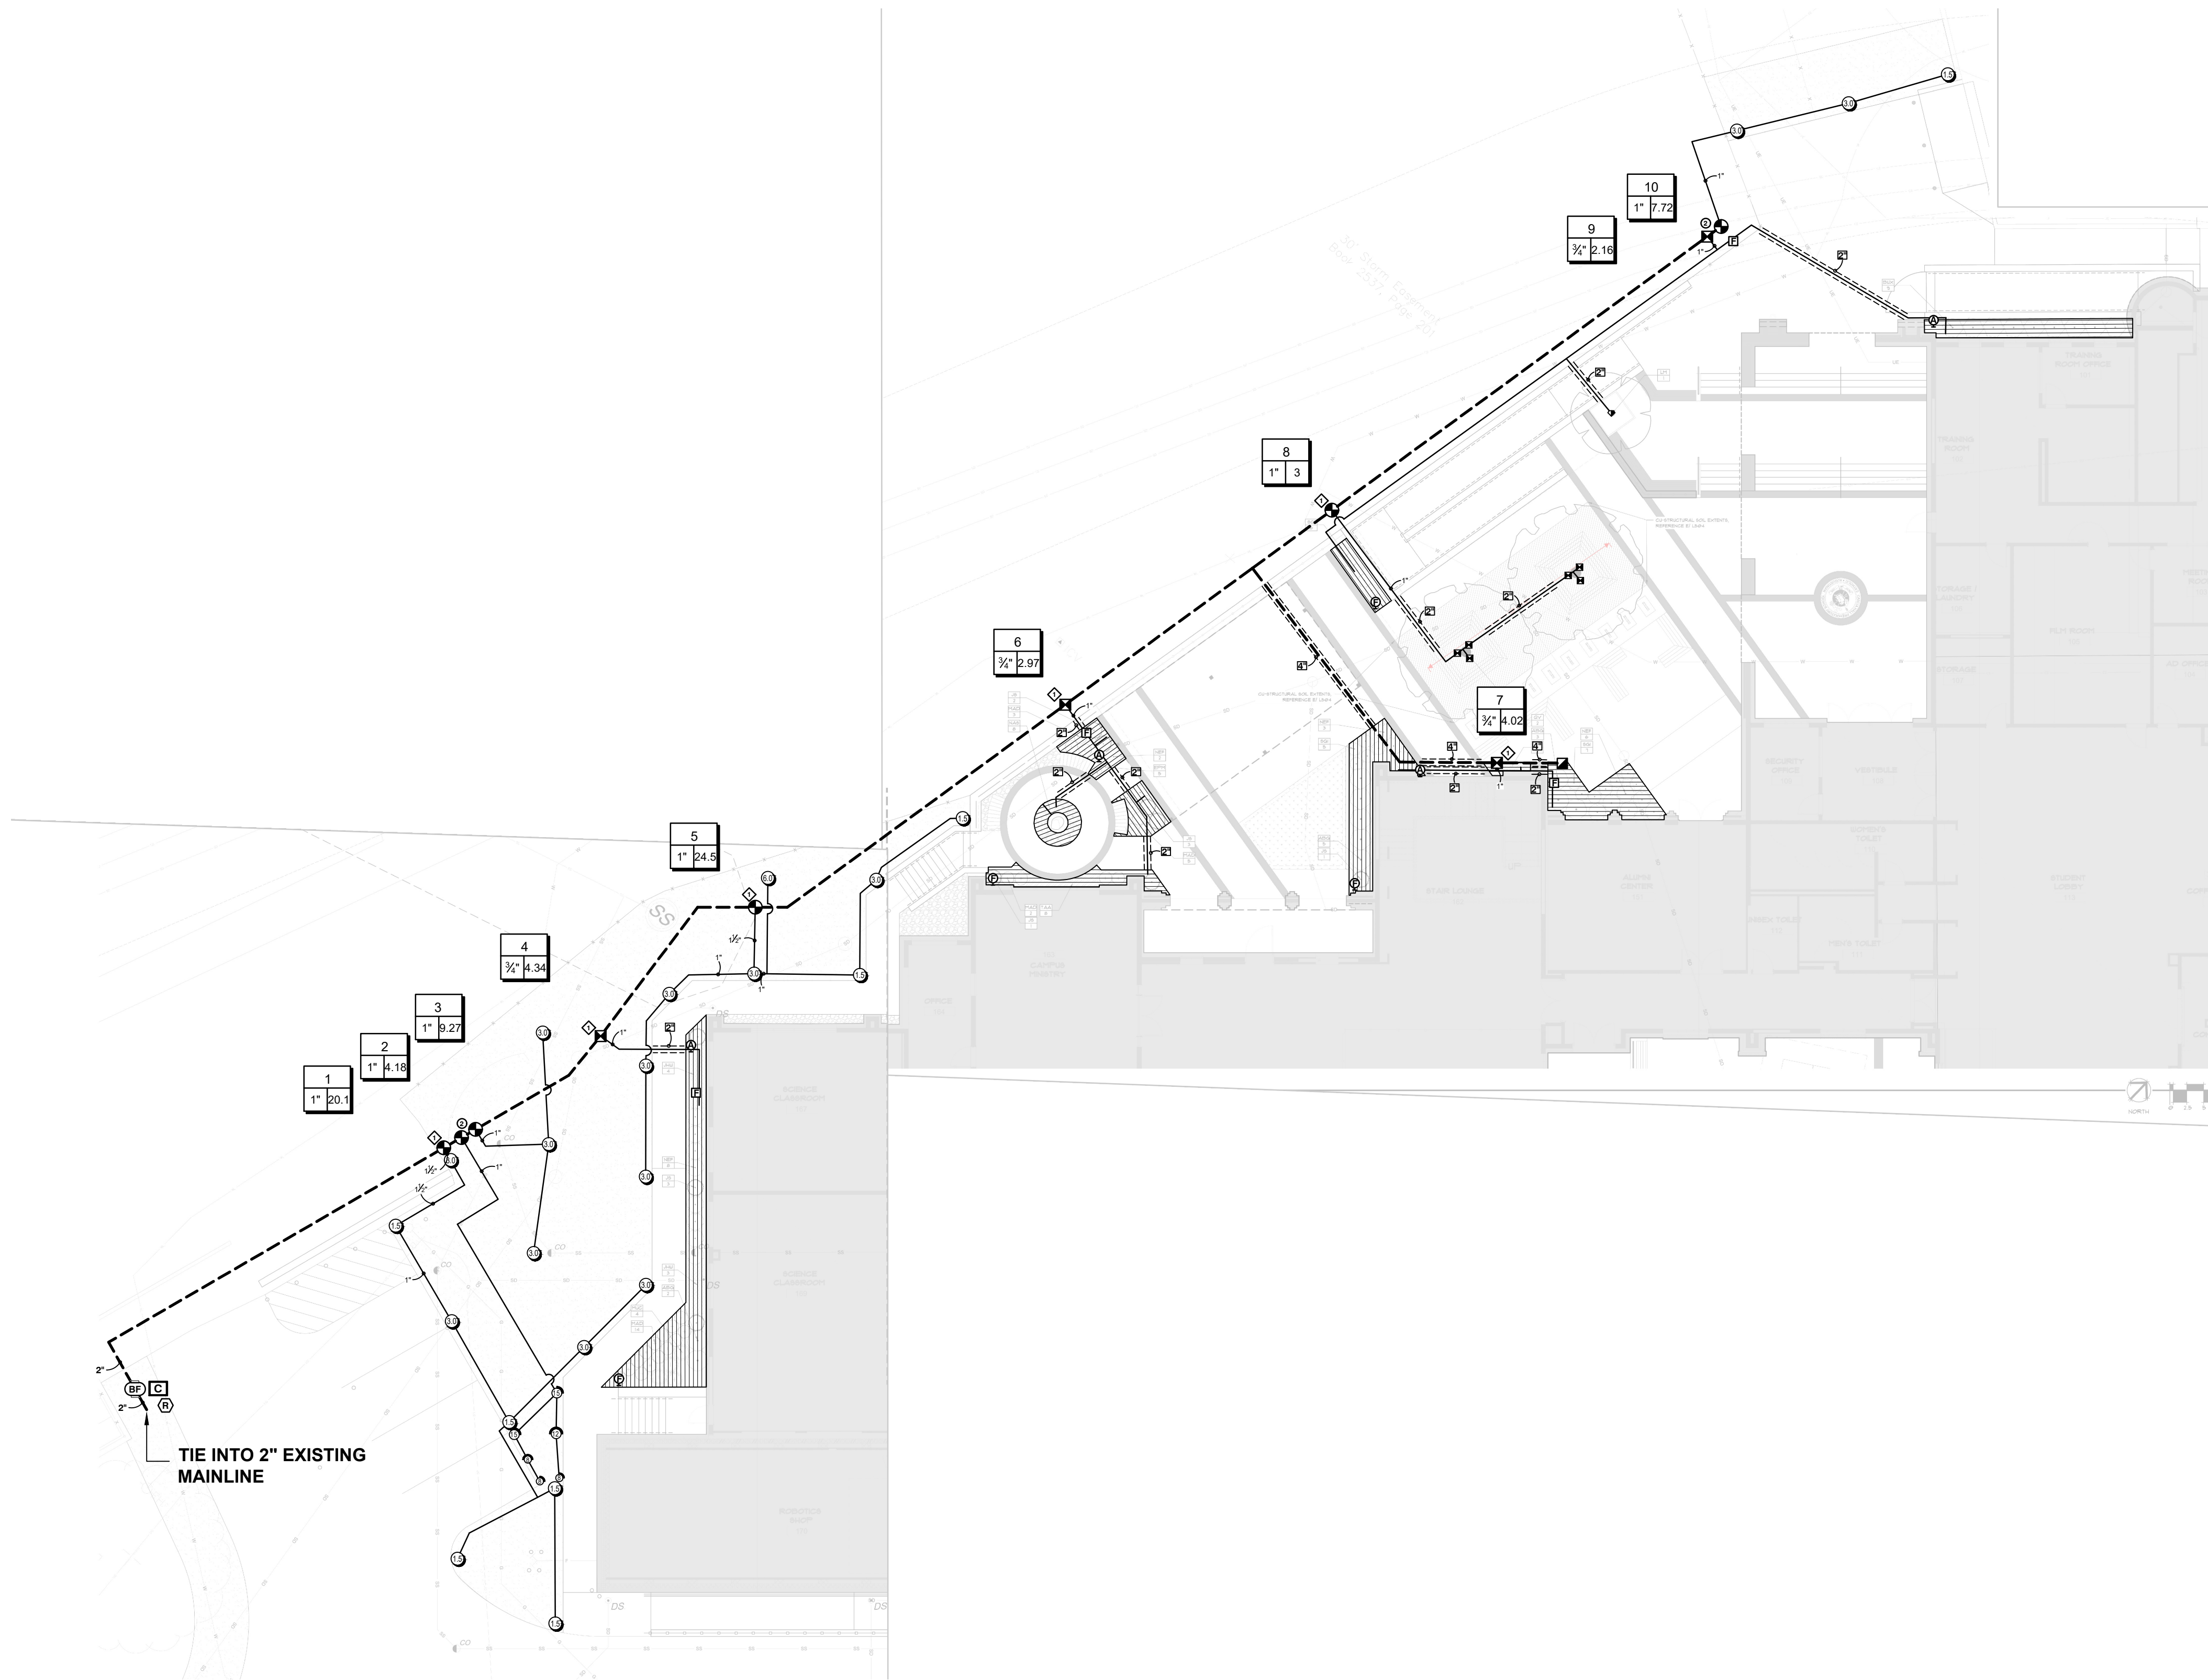


Project Name:
**CASCIA HALL - STEM / STUDENT
LIFE ADDITION**
TULSA, OK


Customer Name:

Design Date: 04-14-26

Drawn By: TOM

REVISIONS

Description	Date
△	
△	
△	
△	

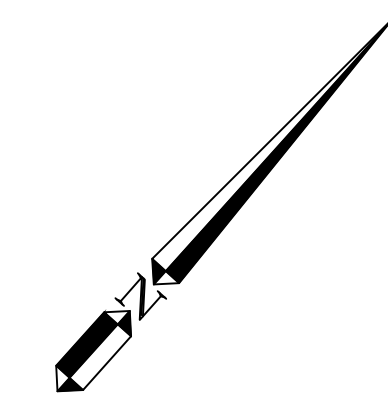

Drawing Scale: 1" = 30'

Project Services Number: XXXX






Drawing Title:

IRRIGATION PLAN

Sheet Number:

IR-1

IRRIGATION SCHEDULE

  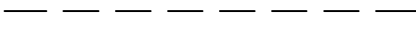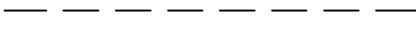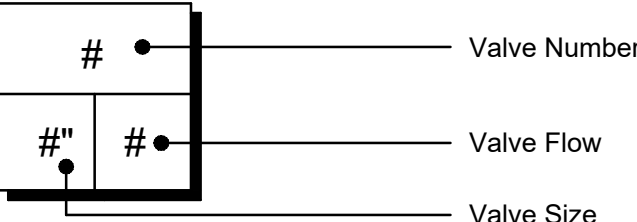SYMBOL	MANUFACTURER/MODEL	QTY
	Rain Bird 1804 08H	1
	Rain Bird 1804 08Q	2
	Rain Bird 1804 12H	1
	Rain Bird 1804 15Q	2
	Rain Bird RWS-B-C 1402	6
SYMBOL	MANUFACTURER/MODEL	QTY
	Rain Bird 5004-PC 1.5	8
	Rain Bird 5004-PC 3.0	14
	Rain Bird 5004-PC 6.0	1
SYMBOL	MANUFACTURER/MODEL	QTY
	Rain Bird XCZ-075-PRF 3/4"	4
	Rain Bird MDCFCAP	4
	Rain Bird ARV050 1/2"	4
	Rain Bird XB-PC	1
	Area to Receive Dripline Rain Bird XFS-CV-06-18	2,019 lf
SYMBOL	MANUFACTURER/MODEL	QTY
	Rain Bird PGA Globe 1"	6
	Rain Bird 5-RC 1"	1
	Wilkins by Zurn Elkay Water Solutions 975XL 1"	1
	Rain Bird ESP-2WIRE	1
	Rain Bird FD-101TURF	6
	Rain Bird FD-202TURF	2
	Rain Bird WR2-RFC	1
	Rain Bird PRB-100 1"	4
	Irrigation Lateral Line: PVC Class 200 SDR 21 1"	1,387 lf
	Irrigation Lateral Line: PVC Class 200 SDR 21 1 1/2"	60.4 lf
	Irrigation Mainline: PVC Class 200 SDR 21 2"	738.0 lf
	Pipe Sleeve: PVC Schedule 40 2"	169.3 lf
	Pipe Sleeve: PVC Schedule 40 4"	74.9 lf
Valve Callout		
	Valve Number Valve Flow Valve Size	

VALVE SCHEDULE

NUMBER	MODEL	SIZE	TYPE	GPM	WIRE	FRICTION LOSS	PSI	PRECIP
1	Rain Bird PGA Globe	1"	Turf Rotor	20.06	144.9	2.56	53.6	0.66 in/h
2	Rain Bird PGA Globe	1"	Turf Spray	4.18	151.0	0.3	35.7	1.11 in/h
3	Rain Bird PGA Globe	1"	Turf Rotor	9.27	155.9	0.4	51.2	0.28 in/h
4	Rain Bird XCZ-075-PRF	3/4"	Area for Dripline	4.34	203.1	0.15	31.8	0.43 in/h
5	Rain Bird PGA Globe	1"	Turf Rotor	24.54	268.4	0.88	52.1	0.59 in/h
6	Rain Bird XCZ-075-PRF	3/4"	Area for Dripline	2.97	380.7	0.04	28.1	0.43 in/h
7	Rain Bird XCZ-075-PRF	3/4"	Area for Dripline	4.02	551.5	0.03	30.8	0.43 in/h
8	Rain Bird PGA Globe	1"	Bubbler	3	479.2	0.12	35.4	2.1 in/h
9	Rain Bird XCZ-075-PRF	3/4"	Drip Emitter	2.16	617.8	0.04	27.3	0.43 in/h
10	Rain Bird PGA Globe	1"	Turf Rotor	7.72	622.9	0.54	51.3	0.61 in/h
Common Wire				738.0				

WATERING SCHEDULE

NUMBER	MODEL	TYPE	PRECIP	SUN	MON	TUE	WED	THU	FRI	SAT	IN./WEEK	MIN./WEEK	GAL./WEEK	GAL./DAY
1	Rain Bird PGA Globe	Turf Rotor	0.66 in/h	14 min	14 min	14 min	14 min	14 min	14 min	14 min	1	92	1,846	264
2	Rain Bird PGA Globe	Turf Spray	1.11 in/h	8 min	8 min	8 min	8 min	8 min	8 min	8 min	1	55	230	32.8
3	Rain Bird PGA Globe	Turf Rotor	0.28 in/h	31 min	31 min	31 min	31 min	31 min	31 min	31 min	1	217	2,012	287
4	Rain Bird XCZ-075-PRF	Area for Dripline	0.43 in/h	21 min	21 min	21 min	21 min	21 min	21 min	21 min	1	141	612	87.4
5	Rain Bird PGA Globe	Turf Rotor	0.59 in/h	15 min	15 min	15 min	15 min	15 min	15 min	15 min	1	102	2,503	358
6	Rain Bird XCZ-075-PRF	Area for Dripline	0.43 in/h	20 min	20 min	20 min	20 min	20 min	20 min	20 min	1	140	416	59.4
7	Rain Bird XCZ-075-PRF	Area for Dripline	0.43 in/h	21 min	21 min	21 min	21 min	21 min	21 min	21 min	1	141	567	81.0
8	Rain Bird PGA Globe	Bubbler	2.1 in/h	5 min	5 min	5 min	5 min	5 min	5 min	5 min	1	29	87	12.4
9	Rain Bird XCZ-075-PRF	Drip Emitter	0.43 in/h	21 min	21 min	21 min	21 min	21 min	21 min	21 min	1	141	305	43.6
10	Rain Bird PGA Globe	Turf Rotor	0.61 in/h	15 min	15 min	15 min	15 min	15 min	15 min	15 min	1	99	764	109
TOTALS:				171	171	171	171	171	171	171		1,157	9,341	1,334

IRRIGATION SPECIFICATIONS

- IRRIGATION SYSTEM DESIGN BASED ON 25 GPM AT 80 PSI.
- IRRIGATION DESIGN IS FROM THE POINT OF CONNECTION(POC)ONLY. THE DESIGN IS BASED ON GALLONS PER MINUTE(GPM)AND POUNDS PER SQUARE INCH(PSI)FURNISHED BY OTHERS.
- IRRIGATION CONTRACTOR IS TO VERIFY POINT OF CONNECTION IN THE FIELD. INSTALLER IS TO CONFIRM THE MINIMUM DISCHARGE REQUIREMENTS OF THE POINT OF CONNECTION AS INDICATED ON THE LEGEND PRIOR TO INSTALLATION.
- THE PRESSURE REQUIREMENT AT THE POINT OF CONNECTION IS BASED ON NO MORE THAN 5 FEET OF ELEVATION CHANGE IN THE AREAS OF IRRIGATION.
- ALL PRODUCTS SHALL BE INSTALLED IN ACCORDANCE WITH THE MANUFACTURER’S RECOMMENDATIONS AND ACCORDING TO LOCAL BUILDING, ELECTRICAL, AND PLUMBING CODES.
- IRRIGATION CONTRACTOR WILL ARRANGE INSPECTIONS REQUIRED BY LOCAL AGENCIES AND ORDINANCES DURING THE COURSE OF CONSTRUCTION AS REQUIRED. ALL WIRING TO BE PER LOCAL CODE. BACKFLOW PREVENTION TO BE PER LOCAL CO
- LOCATION OF IRRIGATION COMPONENTS SHOWN ON DRAWING IS APPROXIMATE. ACT PLACEMENT MAY VERY SLIGHTLY AS REQUIRED TO ACHIEVE FULL, EVEN COVERAGE.
- ALL SPRINKLER HEADS SHALL BE INSTALLED PERPENDICULAR TO FINISH GRADES. EXCEPT AS OTHERWISE INDICATED.
- INSTALL IRRIGATION MAINS WITH A MINIMUM 18” OF COVER BASED ON FINISH GRAD INSTALL IRRIGATION LATERALS WITH MINIMUM 12” OF COVER BASED ON FINISH GRAD
- PIPE LOCATIONS ARE DIAGRAMATIC. VALVES AND MAINLINE SHOWN IN PAVED AREA ARE FOR GRAPHIC CLARITY ONLY.
- THE IRRIGATION CONTRACTOR SHALL COMPLY WITH PIPE SIZES AS INDICATED.
- ALL WIRE SPLICES OR CONNECTIONS SHALL BE MADE WITH APPROVED WATERPROOF WIRE CONNECTIONS AND BE IN A VALVE OR SPLICE BOX.
- ALL CONTROLLER/DECODER WIRE SHALL BE THE 2-WIRE CABLE SPECIFIED BY THE CONTROLLER MANUFACTURER.

Project Name:
CASCIA HALL - STEM / STUDENT LIFE ADDITION
TULSA, OK

Customer Name:

Design Date: 04-14-26

Drawn By: TOM


REVISIONS	
Description	Date
	

Drawing Scale: N.T.S


Project Services Number: XXXX

Drawing Title:
IRRIGATION SCHEDULE AND NOTES


Sheet Number:
IR-2

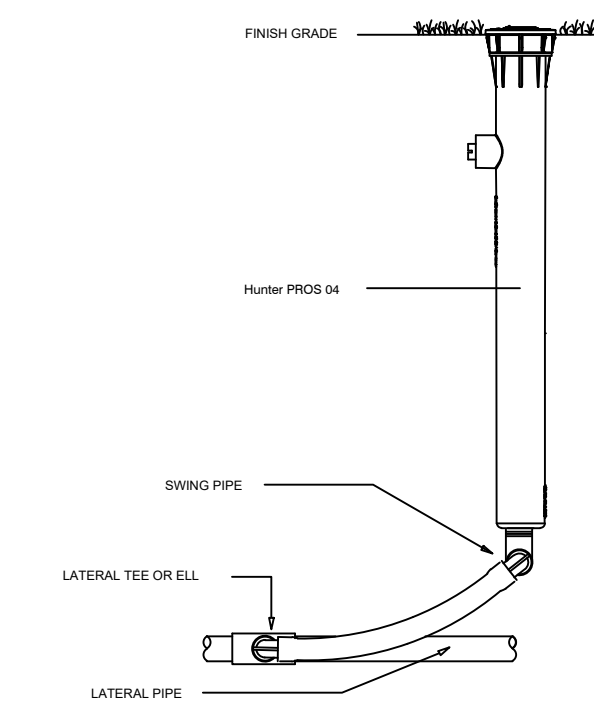


1 POP-UP SPRAY SPRINKLER

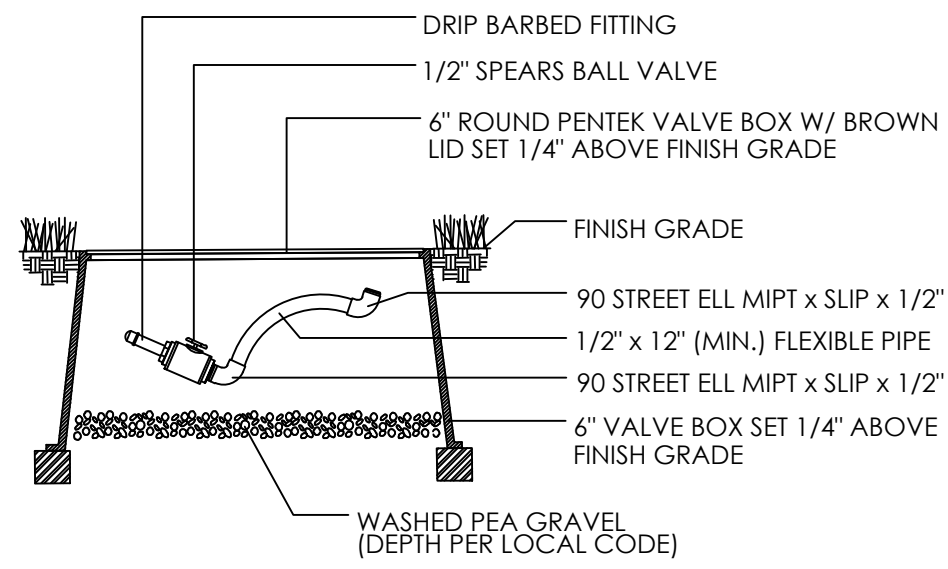


2 FLUSH VALVE

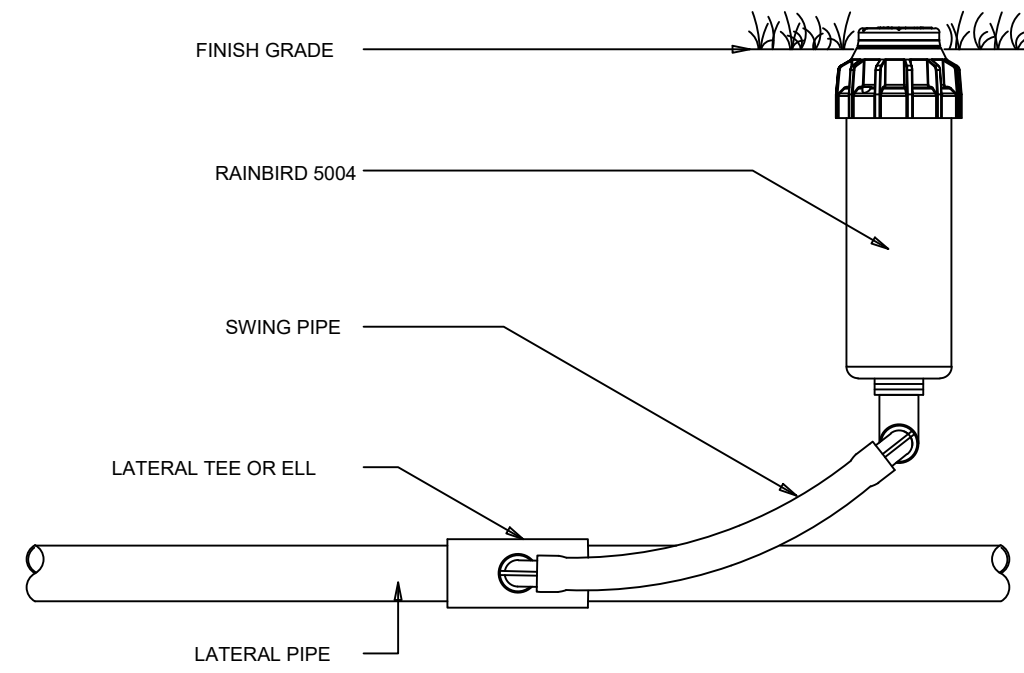


3 ROTOR

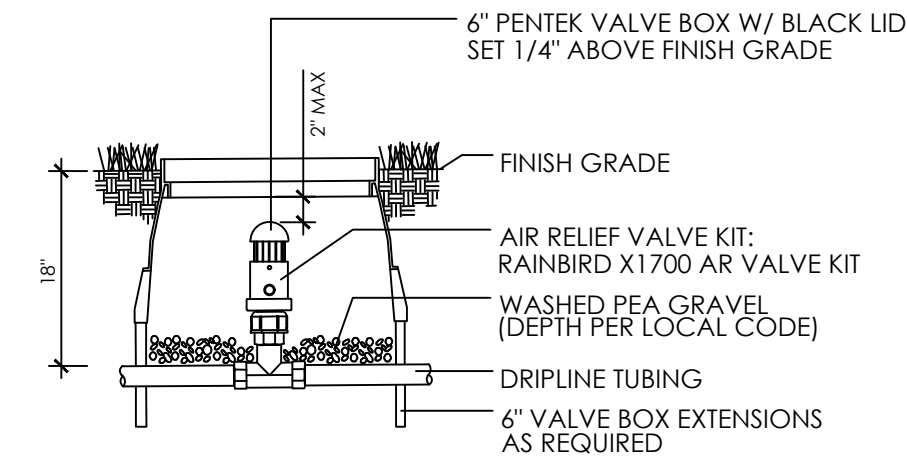


4 AIR RELIEF VALVE

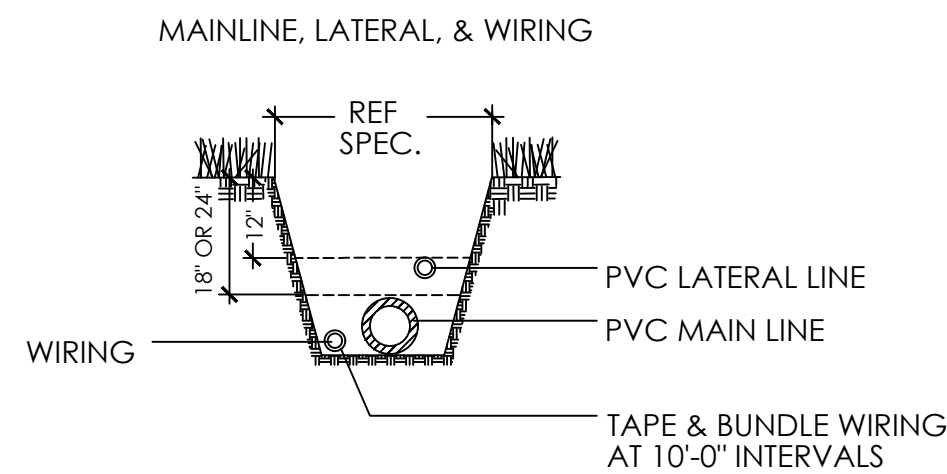


5 TRENCHING DETAIL

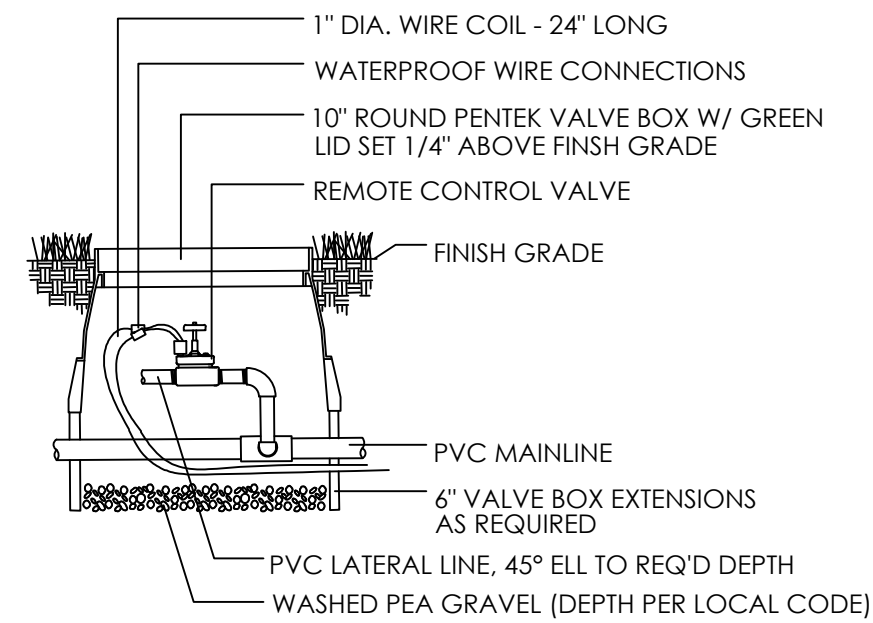


6 REMOTE CONTROL VALVE

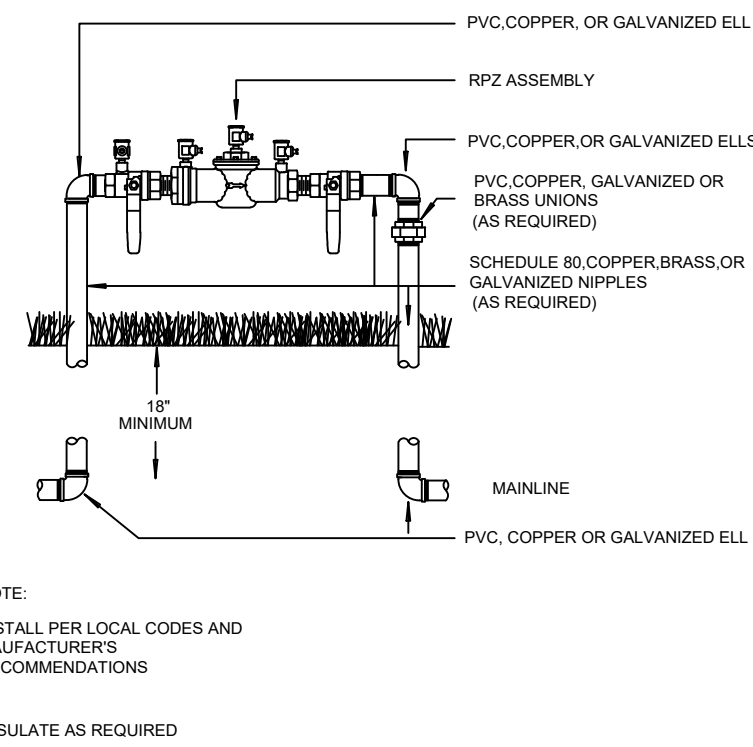

7 RPZ BACKFLOW PREVENTER

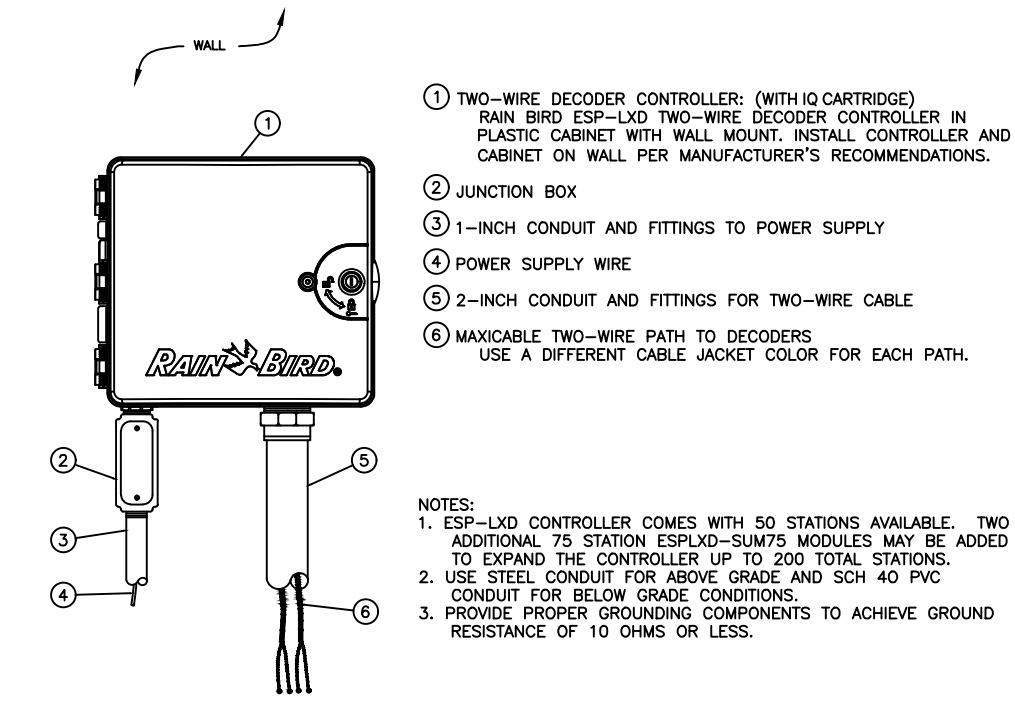

8 ESP-LXD TWO-WIRE DECODER CONTROLLER

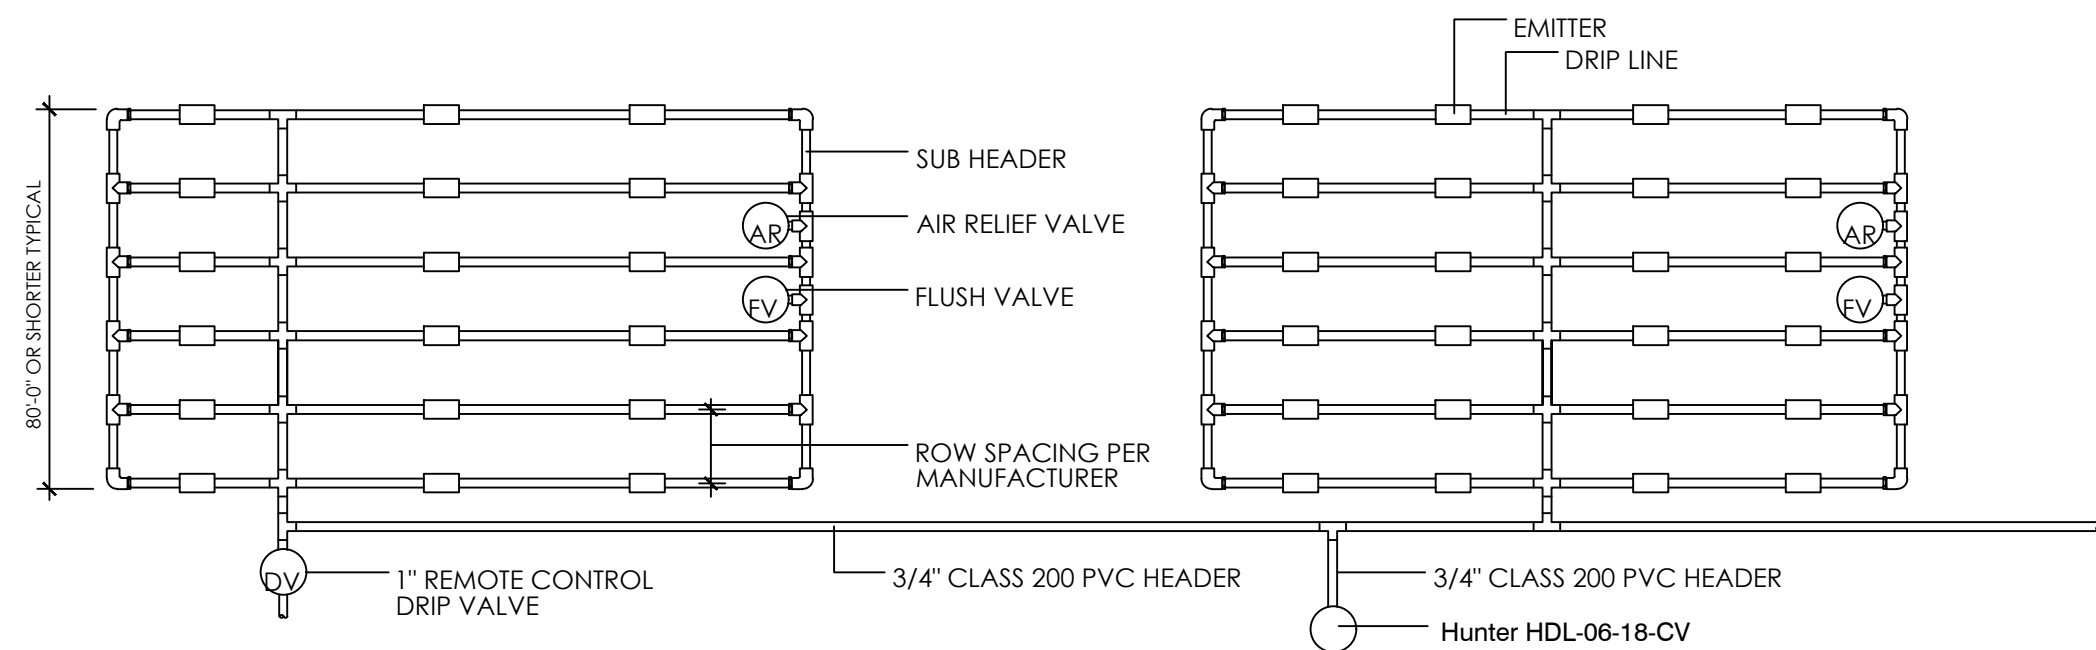

9 TYPICAL DRIP LAYOUT

Project Name:
**CASCIA HALL - STEM / STUDENT
LIFE ADDITION**
TULSA, OK

Customer Name:

Design Date: 04-14-26

Drawn By: TOM

REVISIONS

Description	Date
△	
△	
△	
△	

Drawing Scale: N.T.S

Project Services Number: XXXX

Drawing Title:
IRRIGATION DETAIL SHEET

Sheet Number:
IR-3